


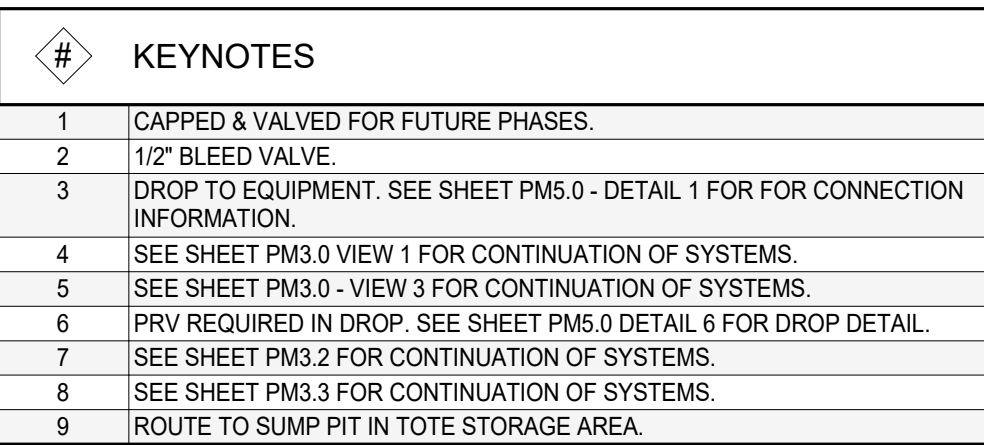

GMA
ARCHITECTS
3113 WOODCREEK DRIVE
DOWNERS GROVE, IL 60515
P: (313) 251-2726
WWW.GMA-ARCHITECTS.COM

ARCO
MURRAY
[DESIGN BUILD]
3113 WOODCREEK DR.
DOWNERS GROVE, IL 60515
P: (313) 251-2726
WWW.ARCOMURRAY.COM

CIVIL
SCOUT & CO
2100 South Tryon Street
Suite 205
Charlotte, NC 28203
(980) 403-2581

STRUCTURAL
ARCO MURRAY ENGINEERING
3113 Woodcreek Dr.
Downers Grove, IL 60515
(331) 251-2726

MECHANICAL, ELECTRICAL, PLUMBING
ASPEN ENGINEERS
14310 Decker Dr.
Magnolia, TX 77355
(713) 882-0410

PROCESS MECHANICAL
ARCO MURRAY ENGINEERING
3113 Woodcreek Dr.
Downers Grove, IL 60515
(312) 361-2798

CLEANROOM
MODESS CLEANROOMS
8 N. Main St.
Suite 400
Attleboro, MA 02703
(508) 695-1012

CONTROLS
SECOND ORDER CONTROLS
3113 Woodcreek Dr.
Downers Grove, IL 60515
(312) 251-2726




ABBREVIATIONS

— CDA: COMPRESSED DRY AIR —

BUILDING KEYPLAN	
-------------------------	--

BUILDING KEYPLAN

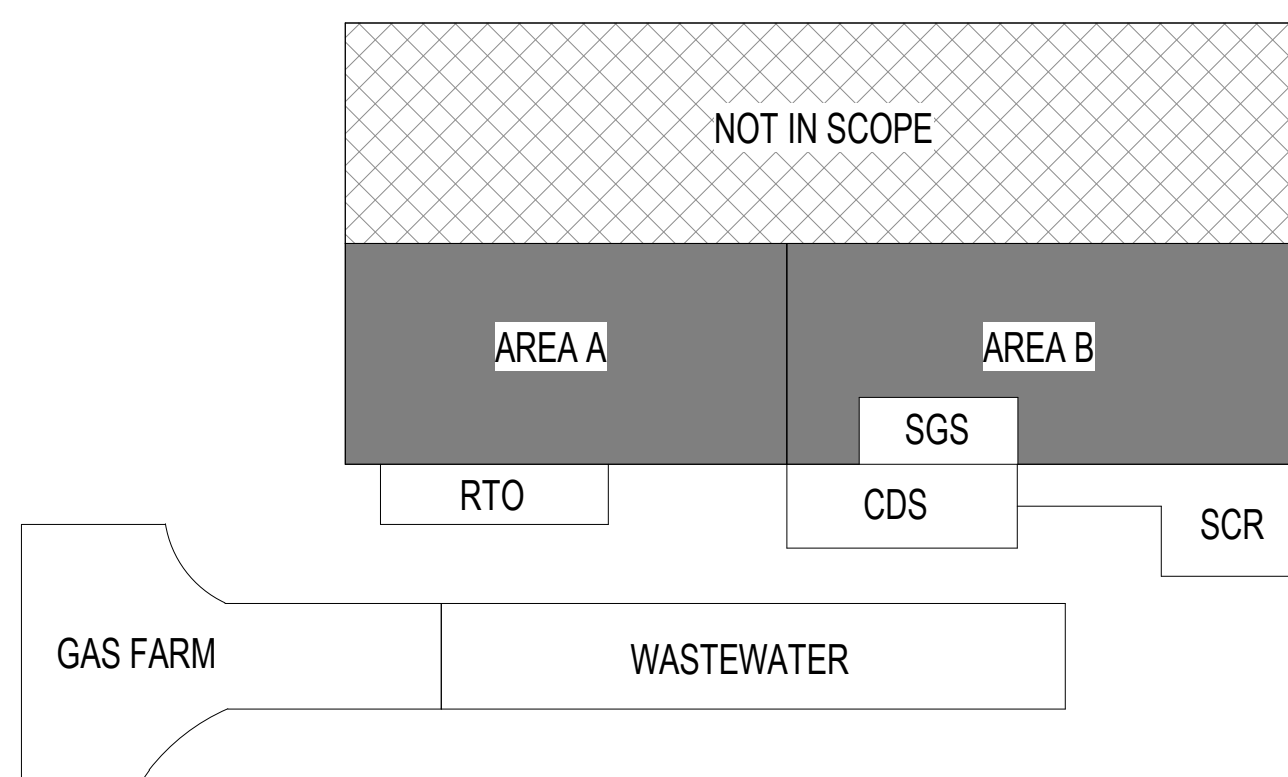

2 PROCESS CDA PIPING PLAN - AREA B
PM2.0 SCALE: 1" = 30'-0"



GMA JOB NO:	-
ARCO JOB NO:	
DRAWN BY:	MFB
ISSUE DATE:	04/29/2026

[illegible]

SHEET NUMBER

PM2.0

PROCESS CDA PIPING PLAN